


Cenário 2 — Falta de água / reservatório vazio

plano-contingencia-agua · Cenário 2 · v0.1 — rascunho para revisão técnica · 2026-10-02 · Nomes e telefones dos níveis 1-2-3: ver a ficha do condomínio

REGRA DE OURO: a reserva técnica de incêndio é intocável, e nenhuma mangueira liga o potável a um circuito.

NUNCA: usar a reserva de incêndio para consumo · ligar bomba a seco · deixar a reposição do chiller ou da torre aberta ao potável durante a falta · beber água de torre, circuito, reúso ou reserva de incêndio · normalizar só porque a água voltou. Ao voltar: reabrir devagar, purgar o ar, descarregar os pontos, conferir cloro, cor, odor e traçador.

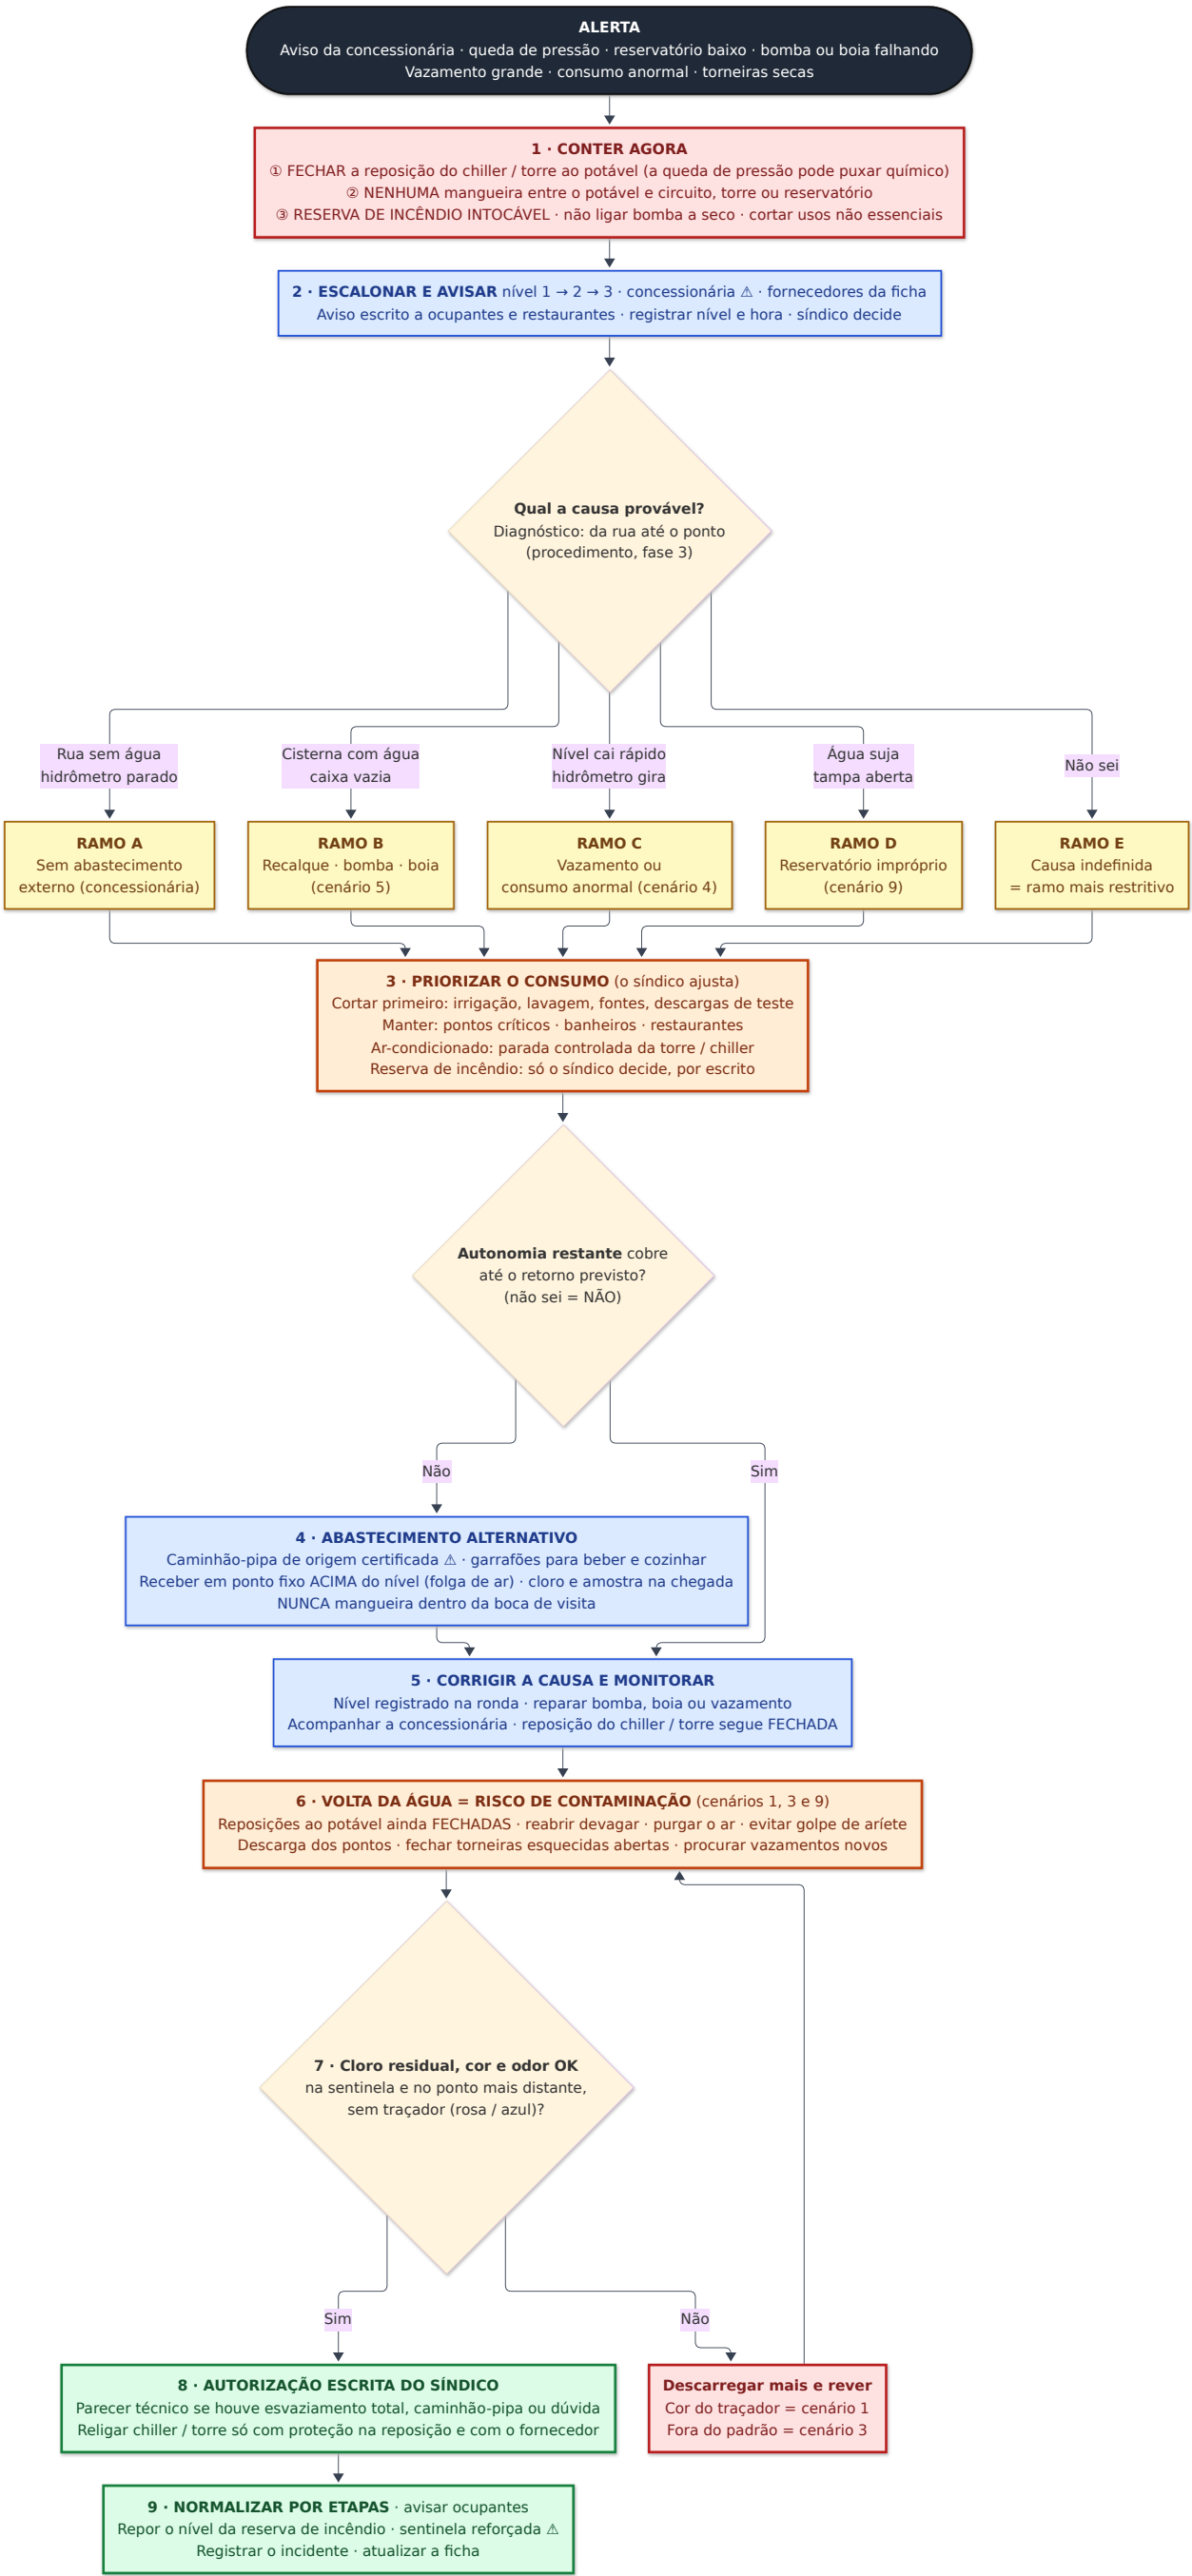

Δ = parâmetro a validar por responsável técnico antes de uso oficial. Este fluxograma não substitui o procedimento completo (cenario-2-falta-de-agua-procedimento.pdf) nem responsável técnico habilitado.