


Cenário 5 — Falha de bomba ou de energia

plano-contingencia-agua · Cenário 5 · v0.1 — rascunho para revisão técnica · 2026-10-02 · Nomes e telefones dos níveis 1-2-3: ver a ficha do condomínio

REGRA DE OURO: segurança de quem opera primeiro. Sem habilitação, ninguém manobra quadro, gerador ou bomba.
NUNCA: tocar em quadro molhado ou com fumaça · forçar rearme repetido · entrar em poço ou área alagada com energia · ligar gerador portátil direto no quadro · gerador em subsolo ou garagem fechada · improvisar mangueira entre potável e circuito. Prioridade: vida, incêndio, drenagem de subsolo, recalque, esgoto, conforto.

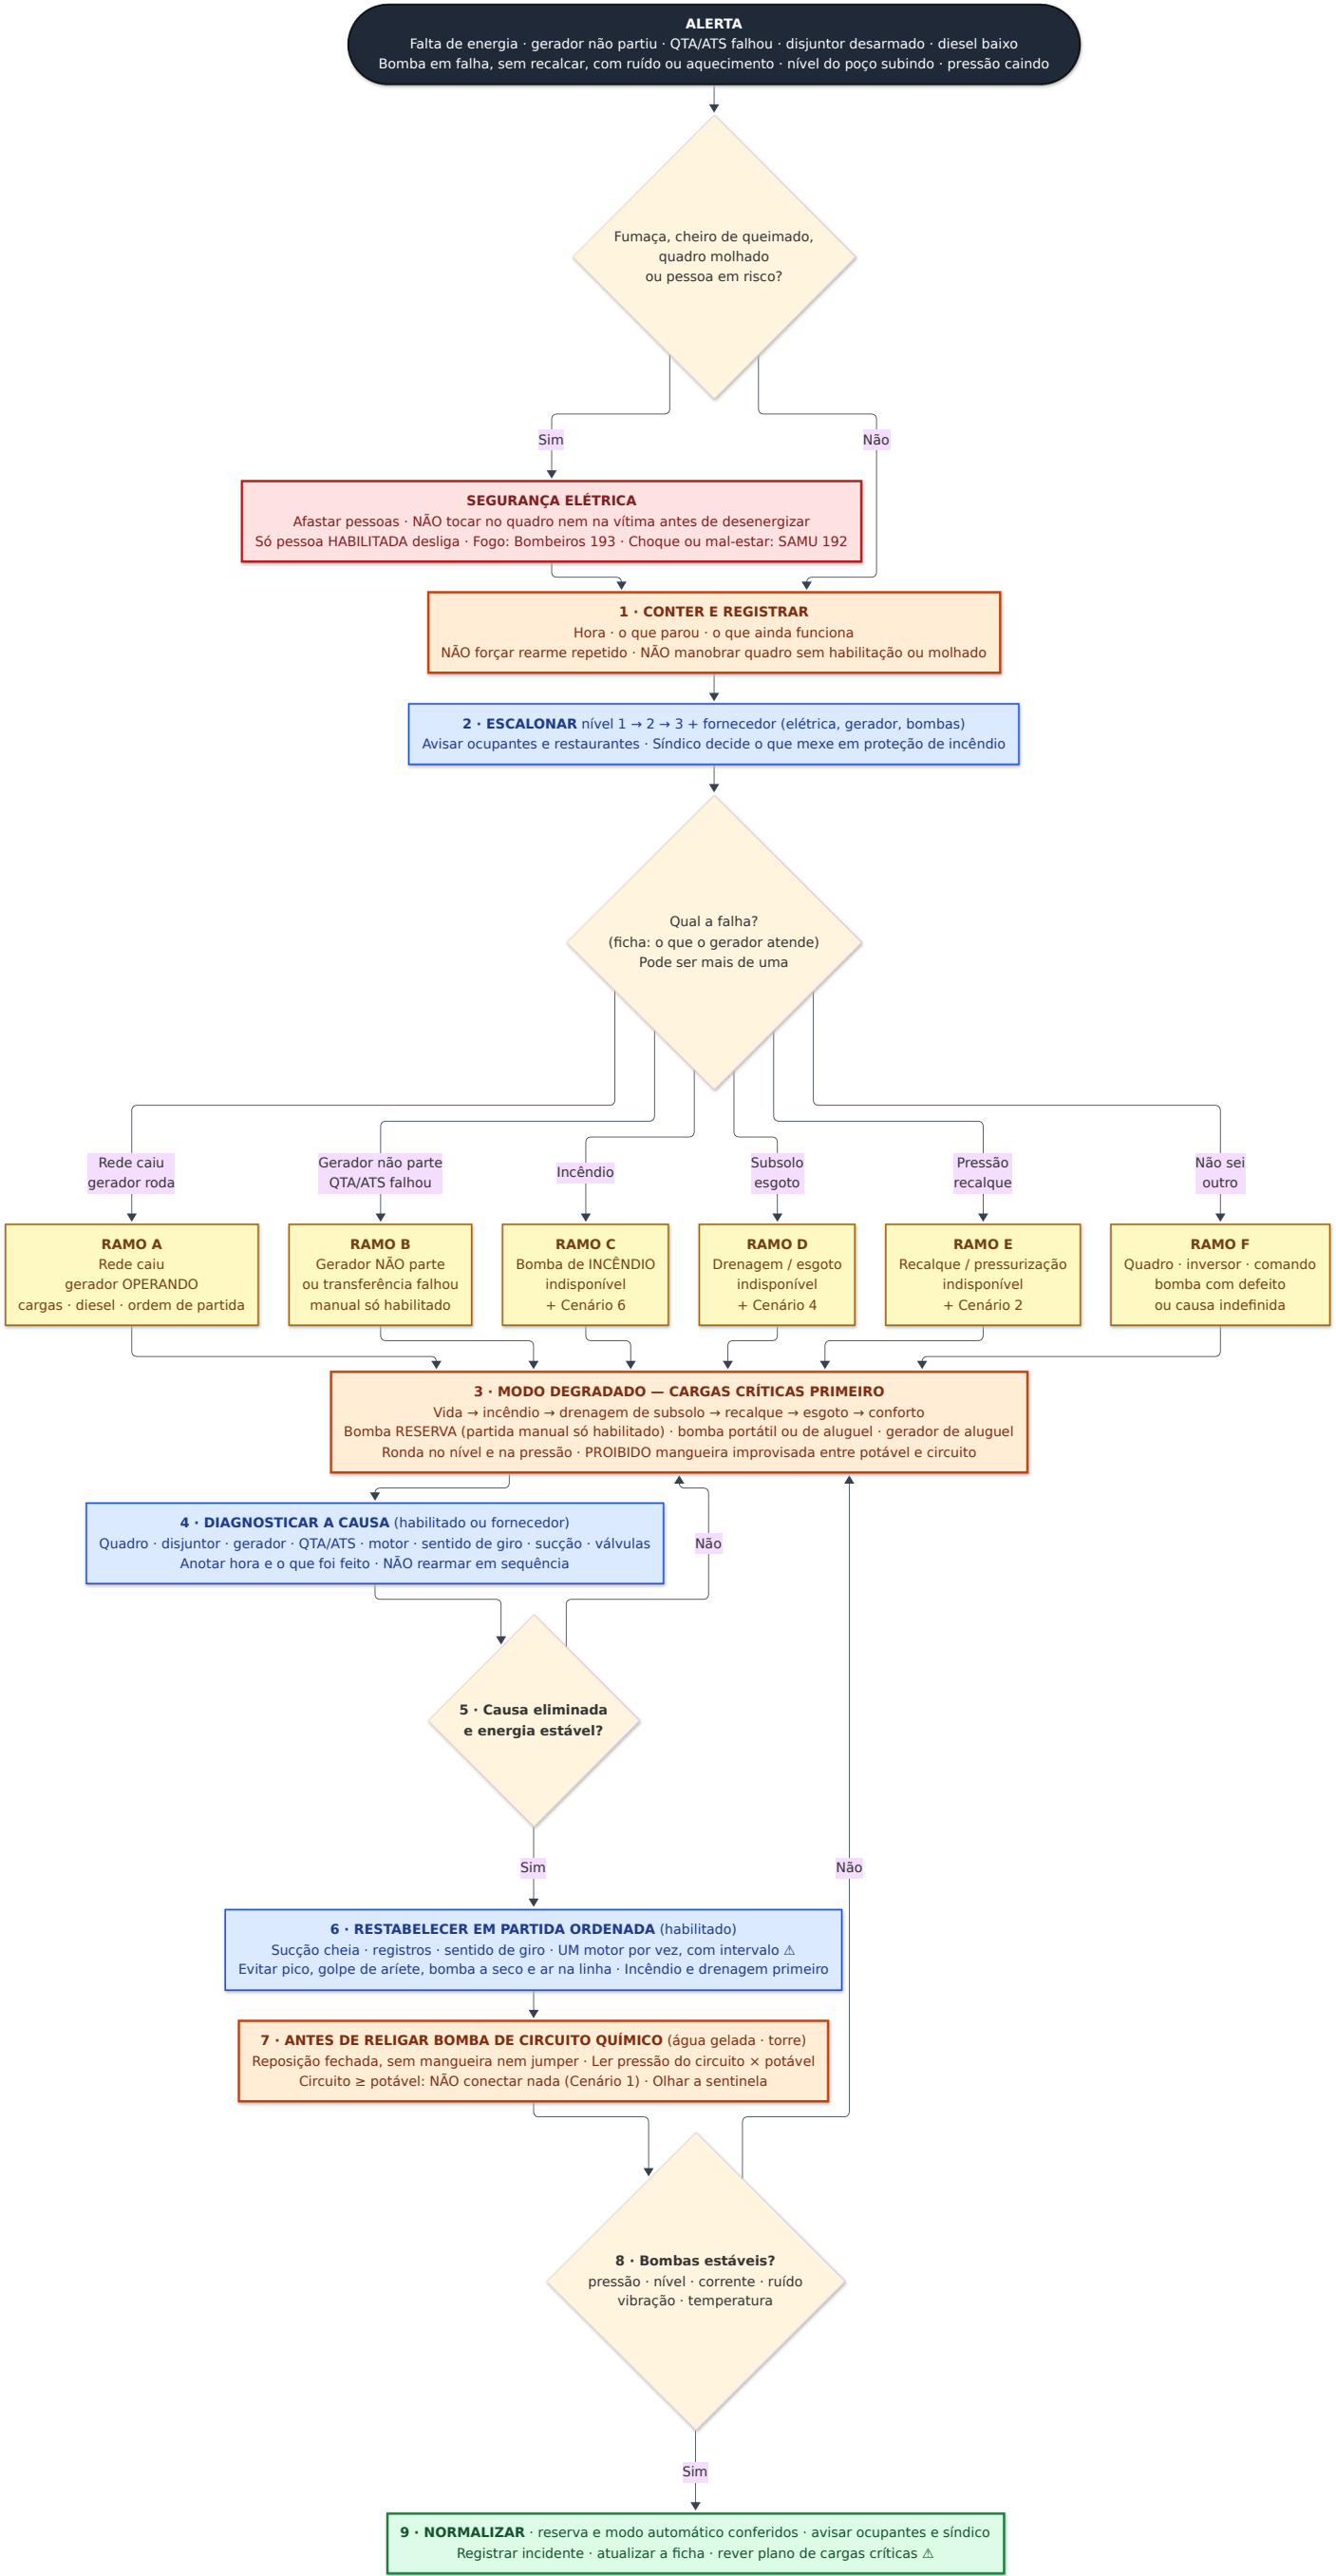

Δ = parâmetro a validar por responsável técnico antes de uso oficial. Este fluxograma não substitui o procedimento completo (cenario-5-falha-de-bomba-ou-energia-procedimento.pdf) nem responsável técnico habilitado.