


Cenário 1 — Contaminação cruzada da água potável

plano-contingencia-agua · Cenário 1 · v0.1 — rascunho para revisão técnica · 2026-10-02 · Nomes e telefones dos níveis 1-2-3: ver a ficha do condomínio

REGRA DE OURO: não pode existir caminho de água contínuo entre o potável e qualquer circuito.

NUNCA: mangueira ligada entre torneira de potável e circuito · descarregar ou limpar antes de coletar · ferver a água · liberar só porque a cor voltou ao normal. Reposição manual segura: o potável enche um TANQUE COM FOLGA DE AR; uma BOMBA leva ao circuito. Antes: ler as pressões; registrar litros; desconectar na hora.

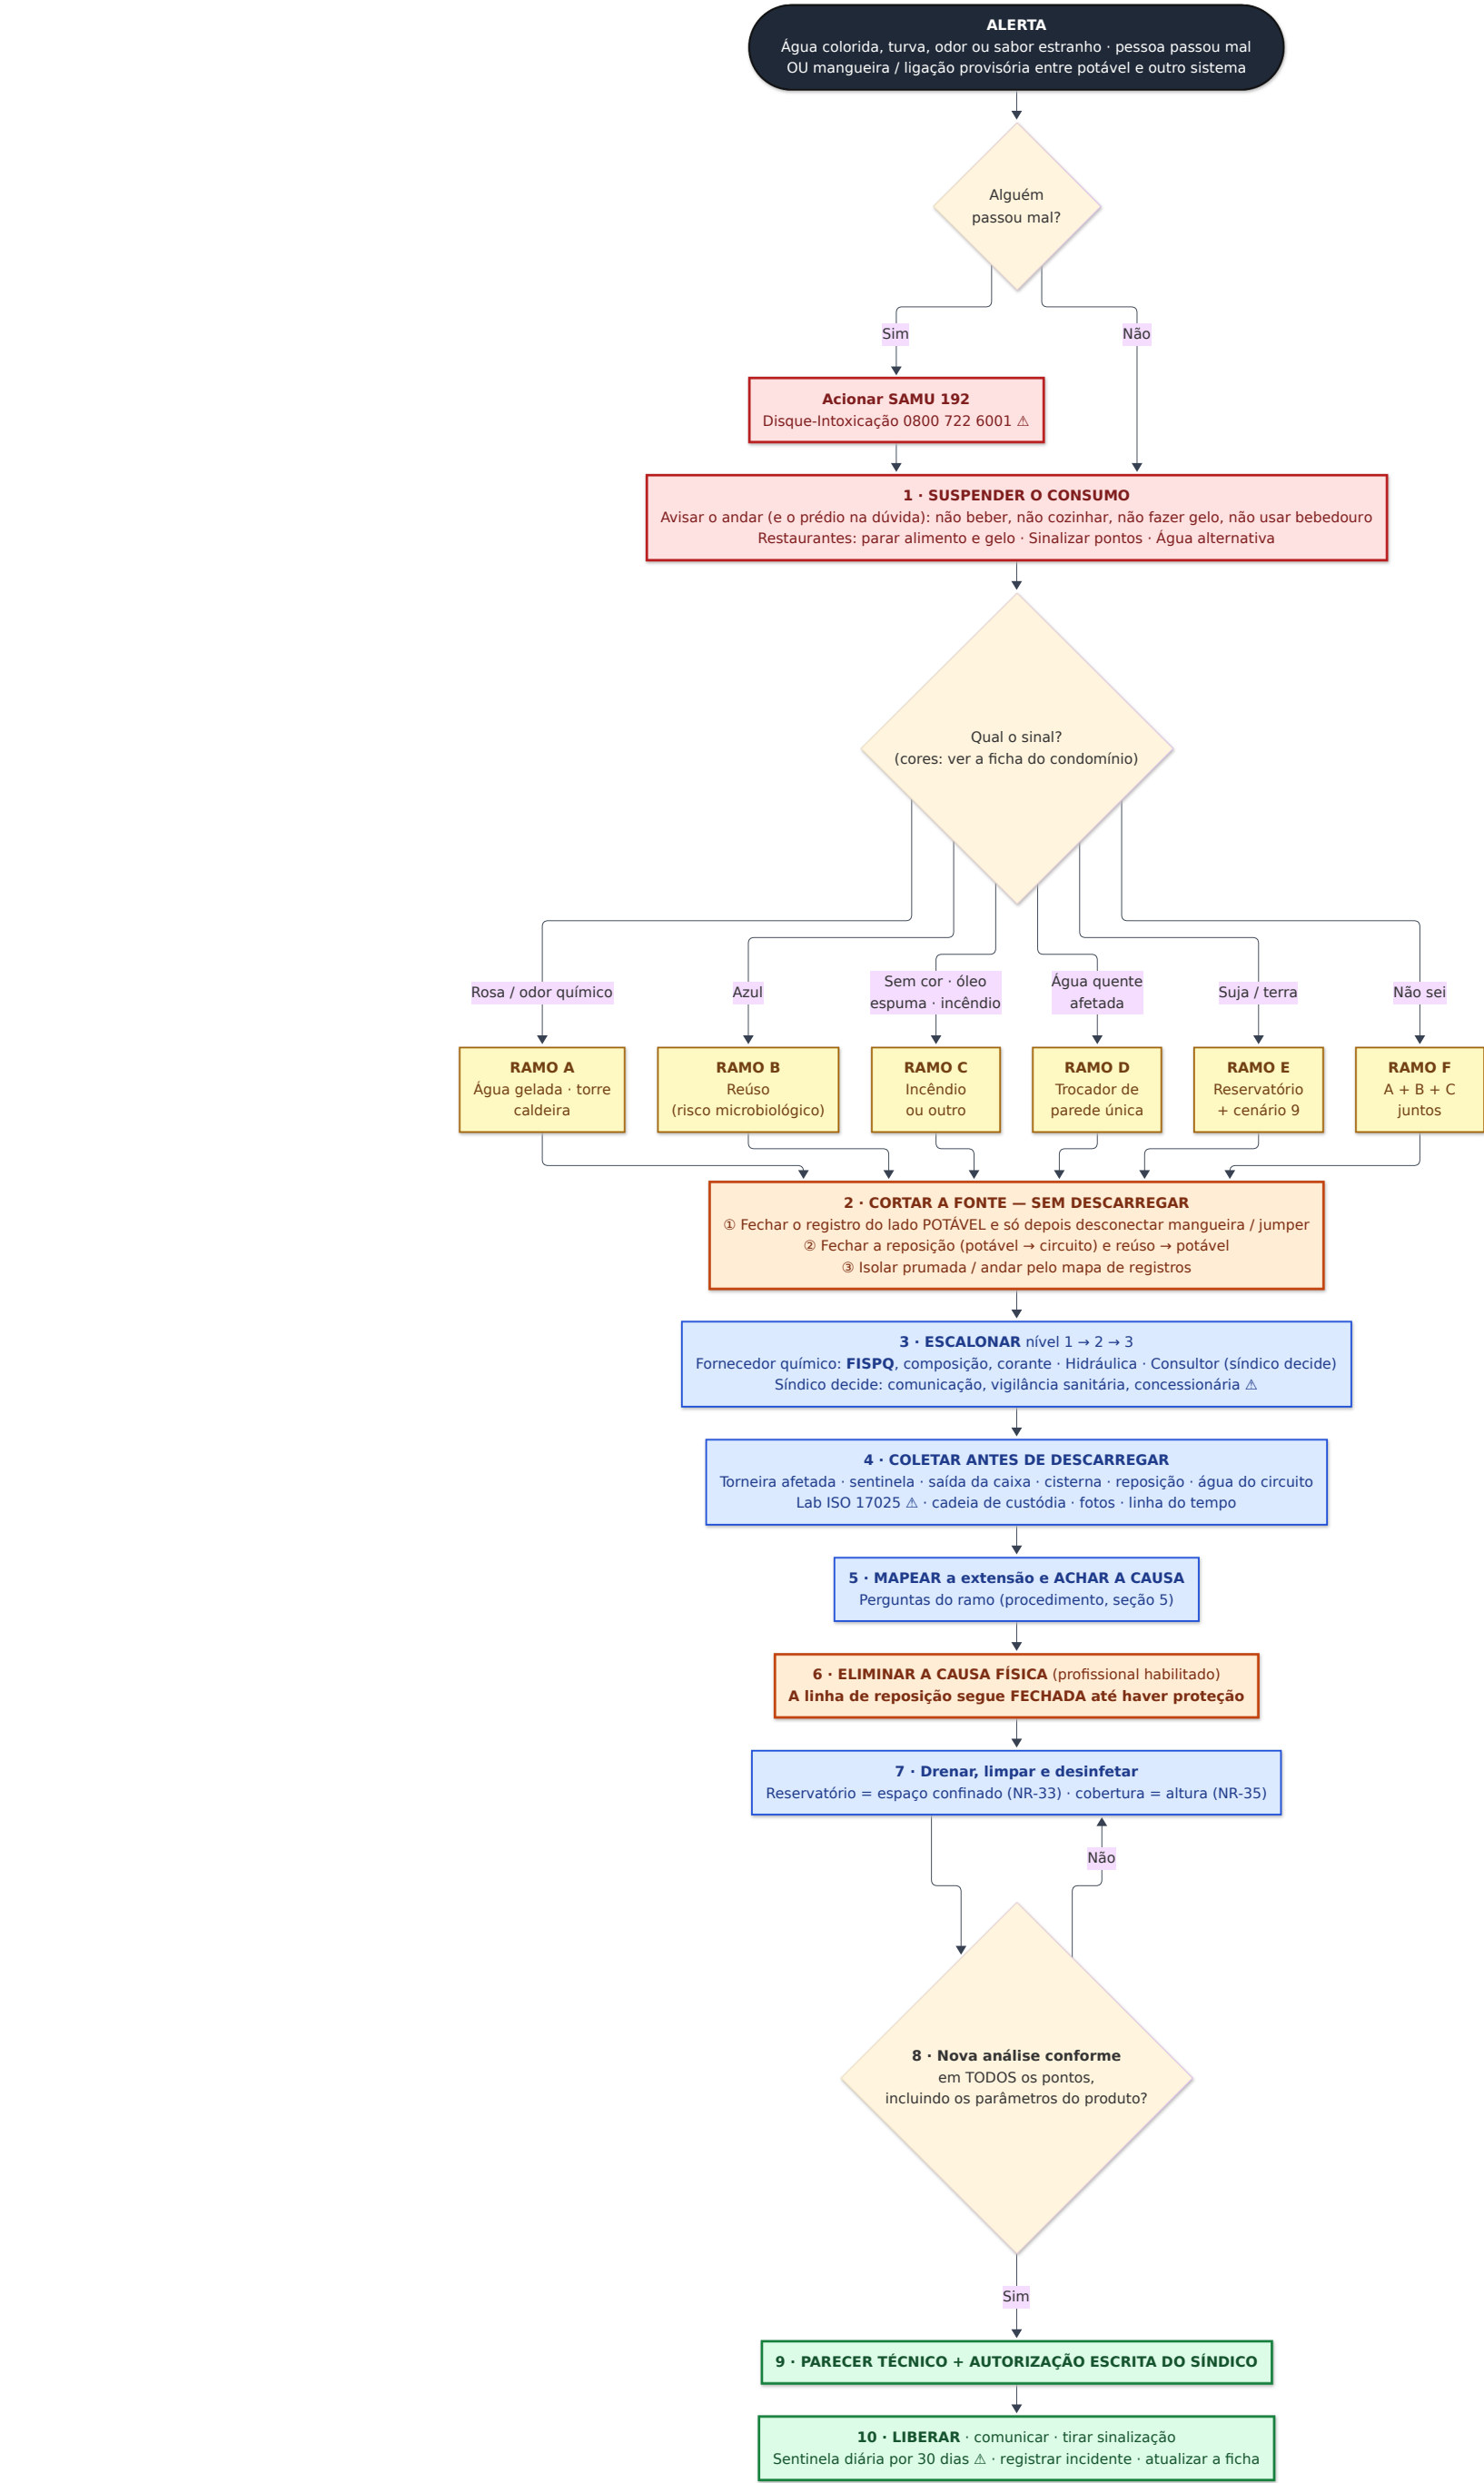

Δ = parâmetro a validar por responsável técnico antes de uso oficial. Este fluxograma não substitui o procedimento completo (procedimento.pdf) nem responsável técnico habilitado.